


CONCEPT, NOT FOR FABRICATION


CityTwin · github.com/BoujeeEnjinia1701/citytwin

REV	DESCRIPTION	DATE	BY
P1	Concept sheet	2026-09-26	AC

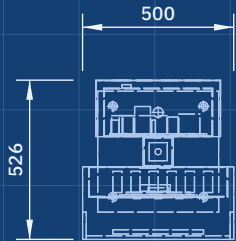

TOP VIEW


Scale 1:25; looking down (along -Z)

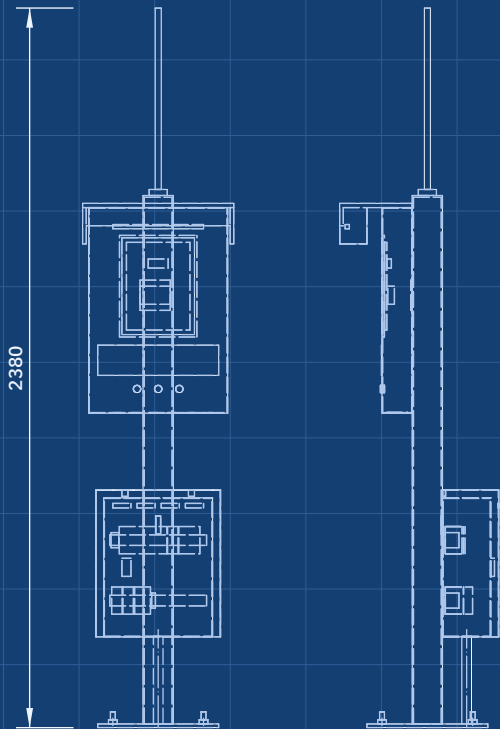

FRONT VIEW

RIGHT VIEW

Scale 1:25; looking at the front (along -Y) Scale 1:25; looking at the right side (along -X)

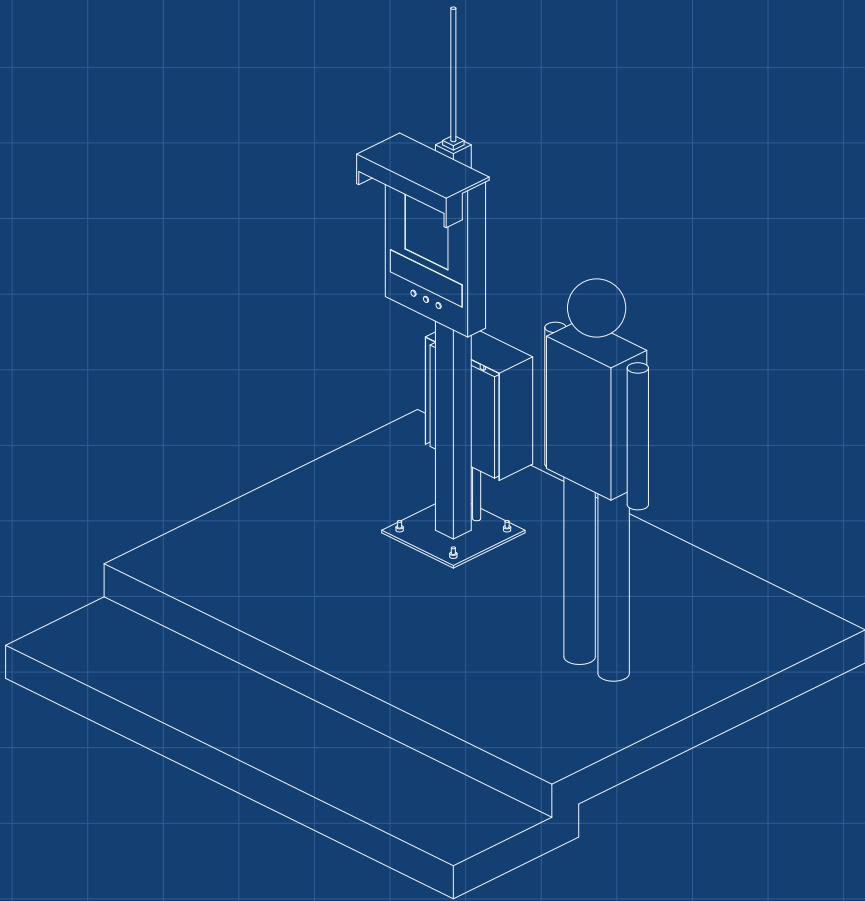

ISOMETRIC VIEW

Not to scale; grey is for scale; seen from the front right and above, about 30 deg elevation

KEY FIGURES

Reference neighborhood: 46 LoRaWAN nodes, 5,616 uplinks a day, 0.61 % lost
13.3 in color e-paper, 1600 x 1200 px, screen center 1.46 m
Buttons at 1.12 m; LED ring at once, layer in 19.8 s (R10: 25 s)
9.2 W average from the mains with TwinKit; about 60 kg with sun shield
Pilot kiosk \$739 (\$750 budget); \$1,029 with TwinKit gateway (indicative)

CITYTWIN

github.com/BoujeeEnjinia1701/citytwin

Public kiosk and data flow concept

DRAWING NO. CTW-DWG-010			REV P1	SHEET 1 of 1	SIZE ANSI B
SCALE 1:25	UNITS mm	PROJECTION 	DATE 2026-09-26	DRAWN Amish Chadha	

MATERIAL / NOTES
Massing model for concept communication